


UV – Schranklayout

Verteilpunkt_SPK_1

Raum: Speisekammer | 5×12 TE | Benutzerdefiniert

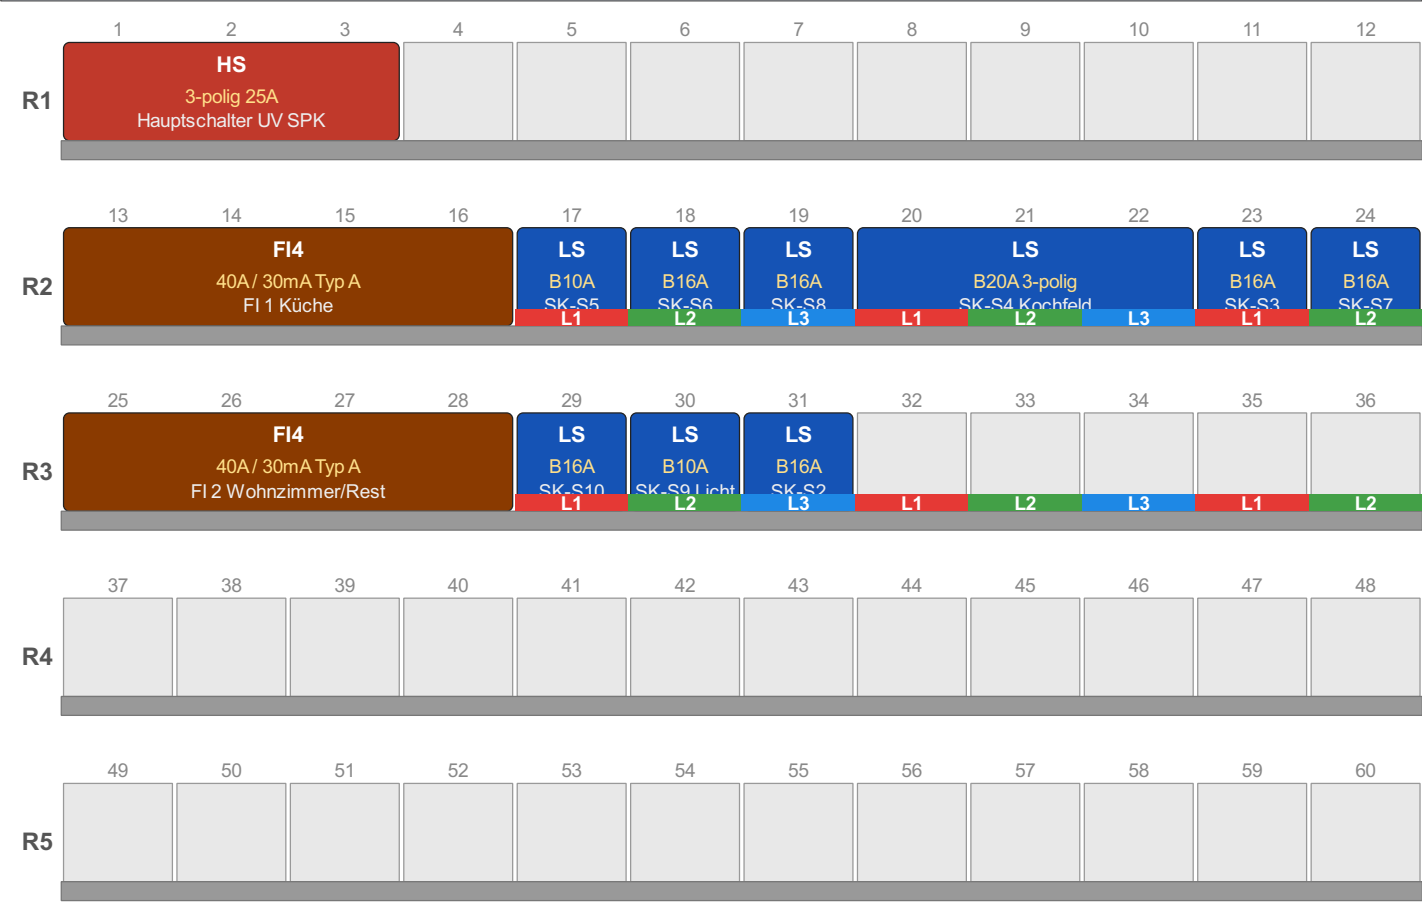

UV – Schranklayout – Belegung

Reihe	TE	Typ	Kennz.	Bezeichnung	Kabel/Stromkreis	Notiz
R1	1	Hauptschalter	3-polig 25A	Hauptschalter UV SPK	Abgang UV HWR Pos 16	Zuleitung von UV HWR
R2	1	FI 4-polig	40A / 30mA Typ A	FI 1 Küche	RCD-Bereich Küche	LS direkt rechts via Phasenschiene
R2	5	LS	B10A	SK-S5 Dunstabzug (L1)	AP-65 VP Küche L1	Kabel im Schritt 2
R2	6	LS	B16A	SK-S6 Geschirrspüler (L2)	AP-65 VP Küche L2	Kabel im Schritt 2
R2	7	LS	B16A	SK-S8 Steckdosen Küche (L3)	AP-65 VP Küche L3	Kabel im Schritt 2
R2	8	LS	B20A 3-polig	SK-S4 Kochfeld	Induktionskochfeld	3~/N/PE 400V
R2	11	LS	B16A	SK-S3 Backofen	Backofen	Einzelkreis 1~
R2	12	LS	B16A	SK-S7 Kühlschrank	Kühlschrank	Einzelkreis 1~
R3	1	FI 4-polig	40A / 30mA Typ A	FI 2 Wohnzimmer/Rest	RCD-Bereich Wohnbereich	LS direkt rechts via Phasenschiene
R3	5	LS	B16A	SK-S10 Steckdosen WZ+Essbereich (L1)	AP-39 VP WZ L1	Kabel im Schritt 2
R3	6	LS	B10A	SK-S9 Licht Küche+Wohnzimmer (L2)	AP-39 VP WZ L2	Kabel im Schritt 2
R3	7	LS	B16A	SK-S2 Windfang Licht+Steckdosen (L3)	AP-39 VP WZ L3	Kabel im Schritt 2